


PROCESS FLOW DIAGRAM - CRUSHING AND GRINDING

DWG RB-4410-PFD-001 Rev B - Ridgeback Concentrator - SYNTHETIC DEMO

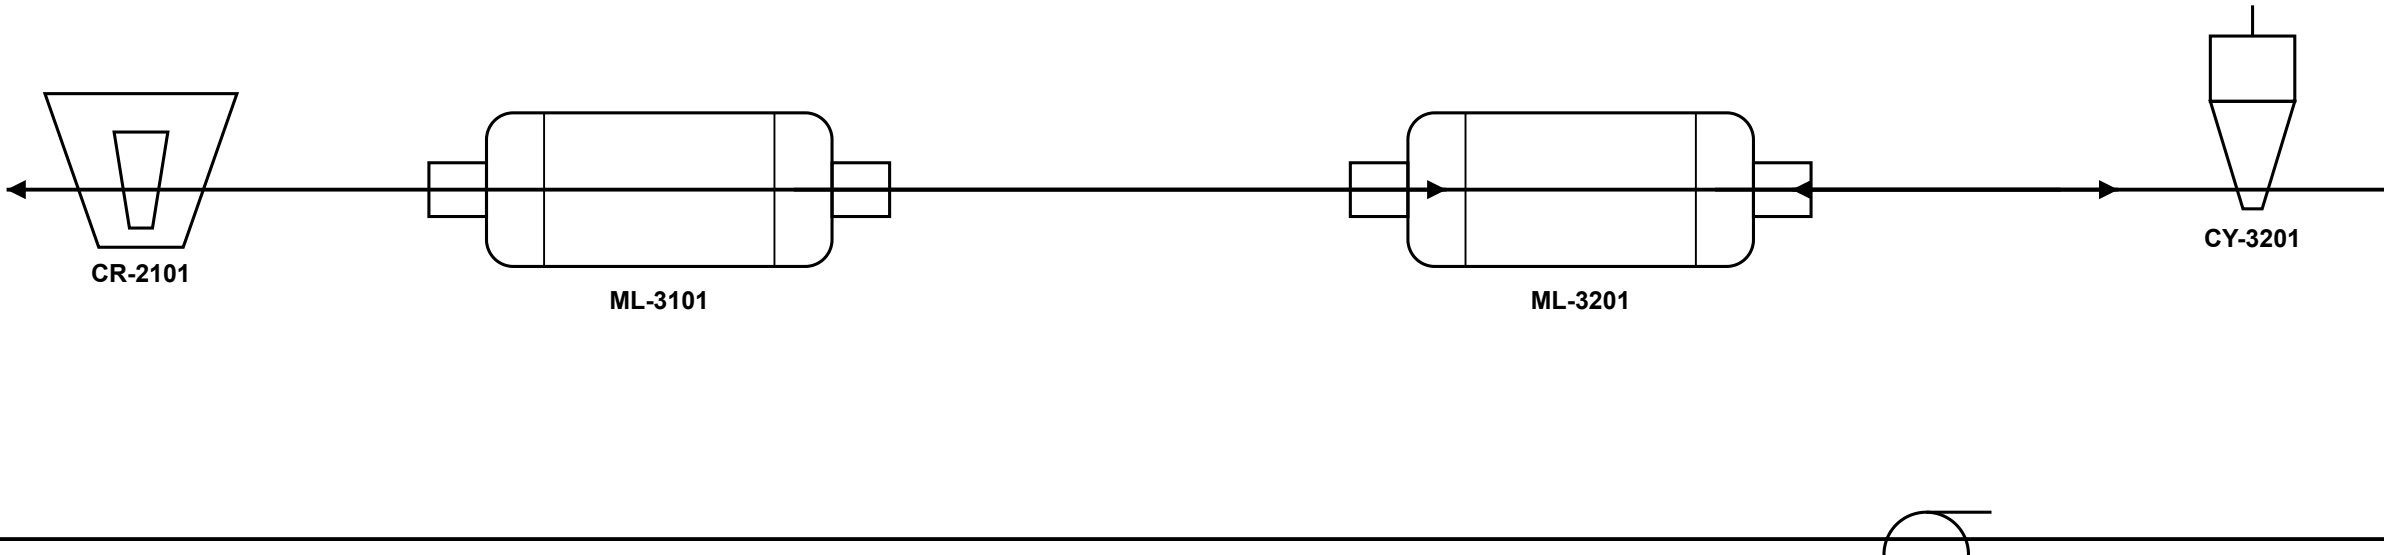

Stream table (design mass balance)

Stream	S-101	S-301	S-305	S-321	S-322	S-323	S-324
Description	Primary crusher product to stockpile	SAG mill fresh feed	Pebble crusher recycle	Cyclone feed (total, 2 duty pumps)	Cyclone feed per duty pump (PP-3201A/B, C standby)	Cyclone underflow to ball mill	Cyclone overflow to flotation
Solids t/h	2688	2688	484	10752	5376	8064	2688
Water t/h	83	83	15	7168	3584	2688	4992
% solids w/w	97.0	97.0	97.0	60.0	60.0	75.0	35.0
Slurry m3/h	1061	1061	191	11078	5539	5620	5969
Slurry SG	2.613	2.613	2.613	1.618	1.618	1.913	1.287

Basis: Circulating load 300 %. Cyclone feed per duty pump 5,539 m3/h at 60.0 % solids (2 duty + 1 standby).