


ML-3101 SAG MILL
Size: 12.2 x 6.7 (40 ft x 22 ft) m
Motor: 20,000 kW GMD
Throughput: 2,688 t/h

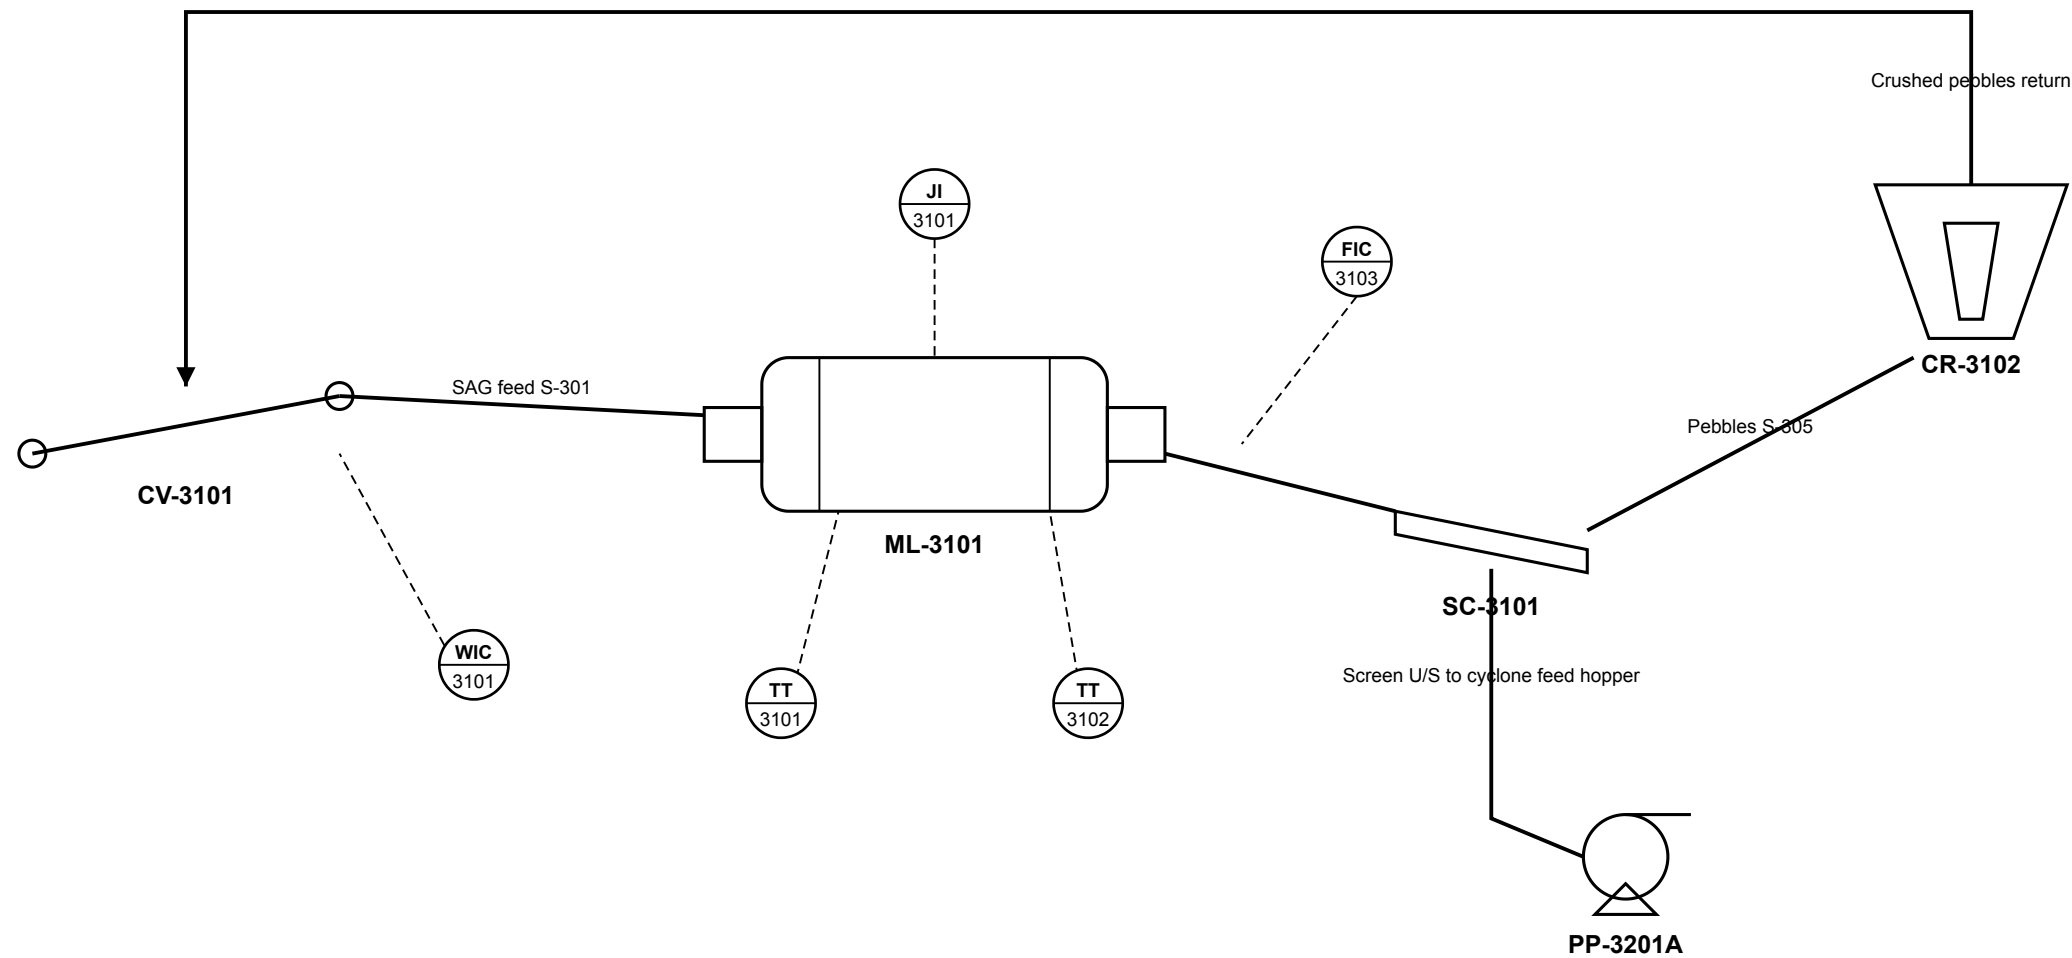

NOTES

1. Hydrostatic lift and lube system on RB-4410-PID-31-002.
2. TT-3101/3102 trip via SIF-3101 - refer RB-4410-STD-CE-001.
3. Mill feed water ratio control FIC-3103 targets 75 % solids in mill.
4. Pebble crusher bypass chute not shown.

Cymbal Copper Pty Ltd (fictional)
Ridgeback Concentrator - Project RB-4410

SYNTHETIC DEMO DRAWING

PIPING & INSTRUMENTATION DIAGRAM
SAG MILL ML-3101

DWG No. RB-4410-PID-31-001

REV B