


TK-3105 LUBE OIL RESERVOIR
Capacity: 12 m3
Oil: ISO VG 460

PP-3105A/B HP LIFT PUMPS
Normal discharge: 120 bar(g)
System design pressure: 170 bar(g)

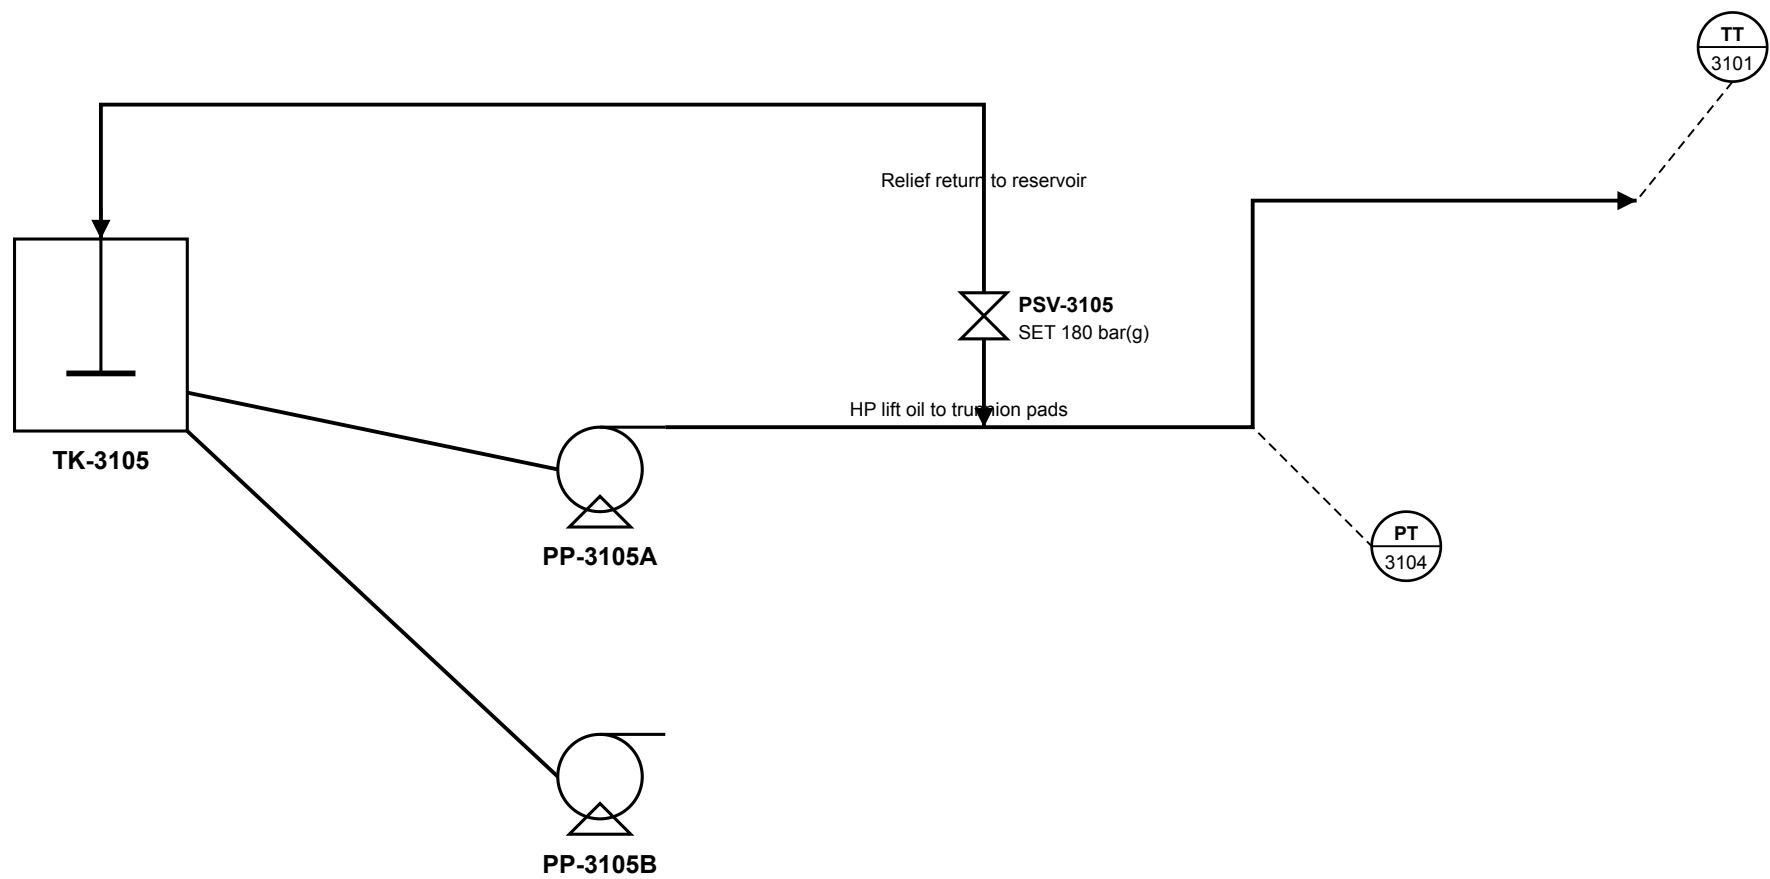

NOTES

1. PSV-3105 protects HP lift pump discharge; set pressure shall not exceed system design pressure.
2. PT-3104 PALL inhibits mill start (SIF-3102).
3. Coolers, filters and heaters not shown.

Cymbal Copper Pty Ltd (fictional)
Ridgeback Concentrator - Project RB-4410

SYNTHETIC DEMO DRAWING

PIPING & INSTRUMENTATION DIAGRAM
SAG MILL HYDROSTATIC LIFT & LUBE SYSTEM

DWG No. RB-4410-PID-31-002

REV B