


ML-3201 BALL MILL
Size: 8.2 x 13.4 (27 ft x 44 ft) m
Motor: 22,000 kW GMD

PP-3201A/B/C CYCLONE FEED PUMPS
2 duty + 1 standby (C not shown)
Rated: 5,539 m3/h each @ SG 1.618

CY-3201 CYCLONE CLUSTER
16 x 660 mm
Feed density: 60.0 % w/w

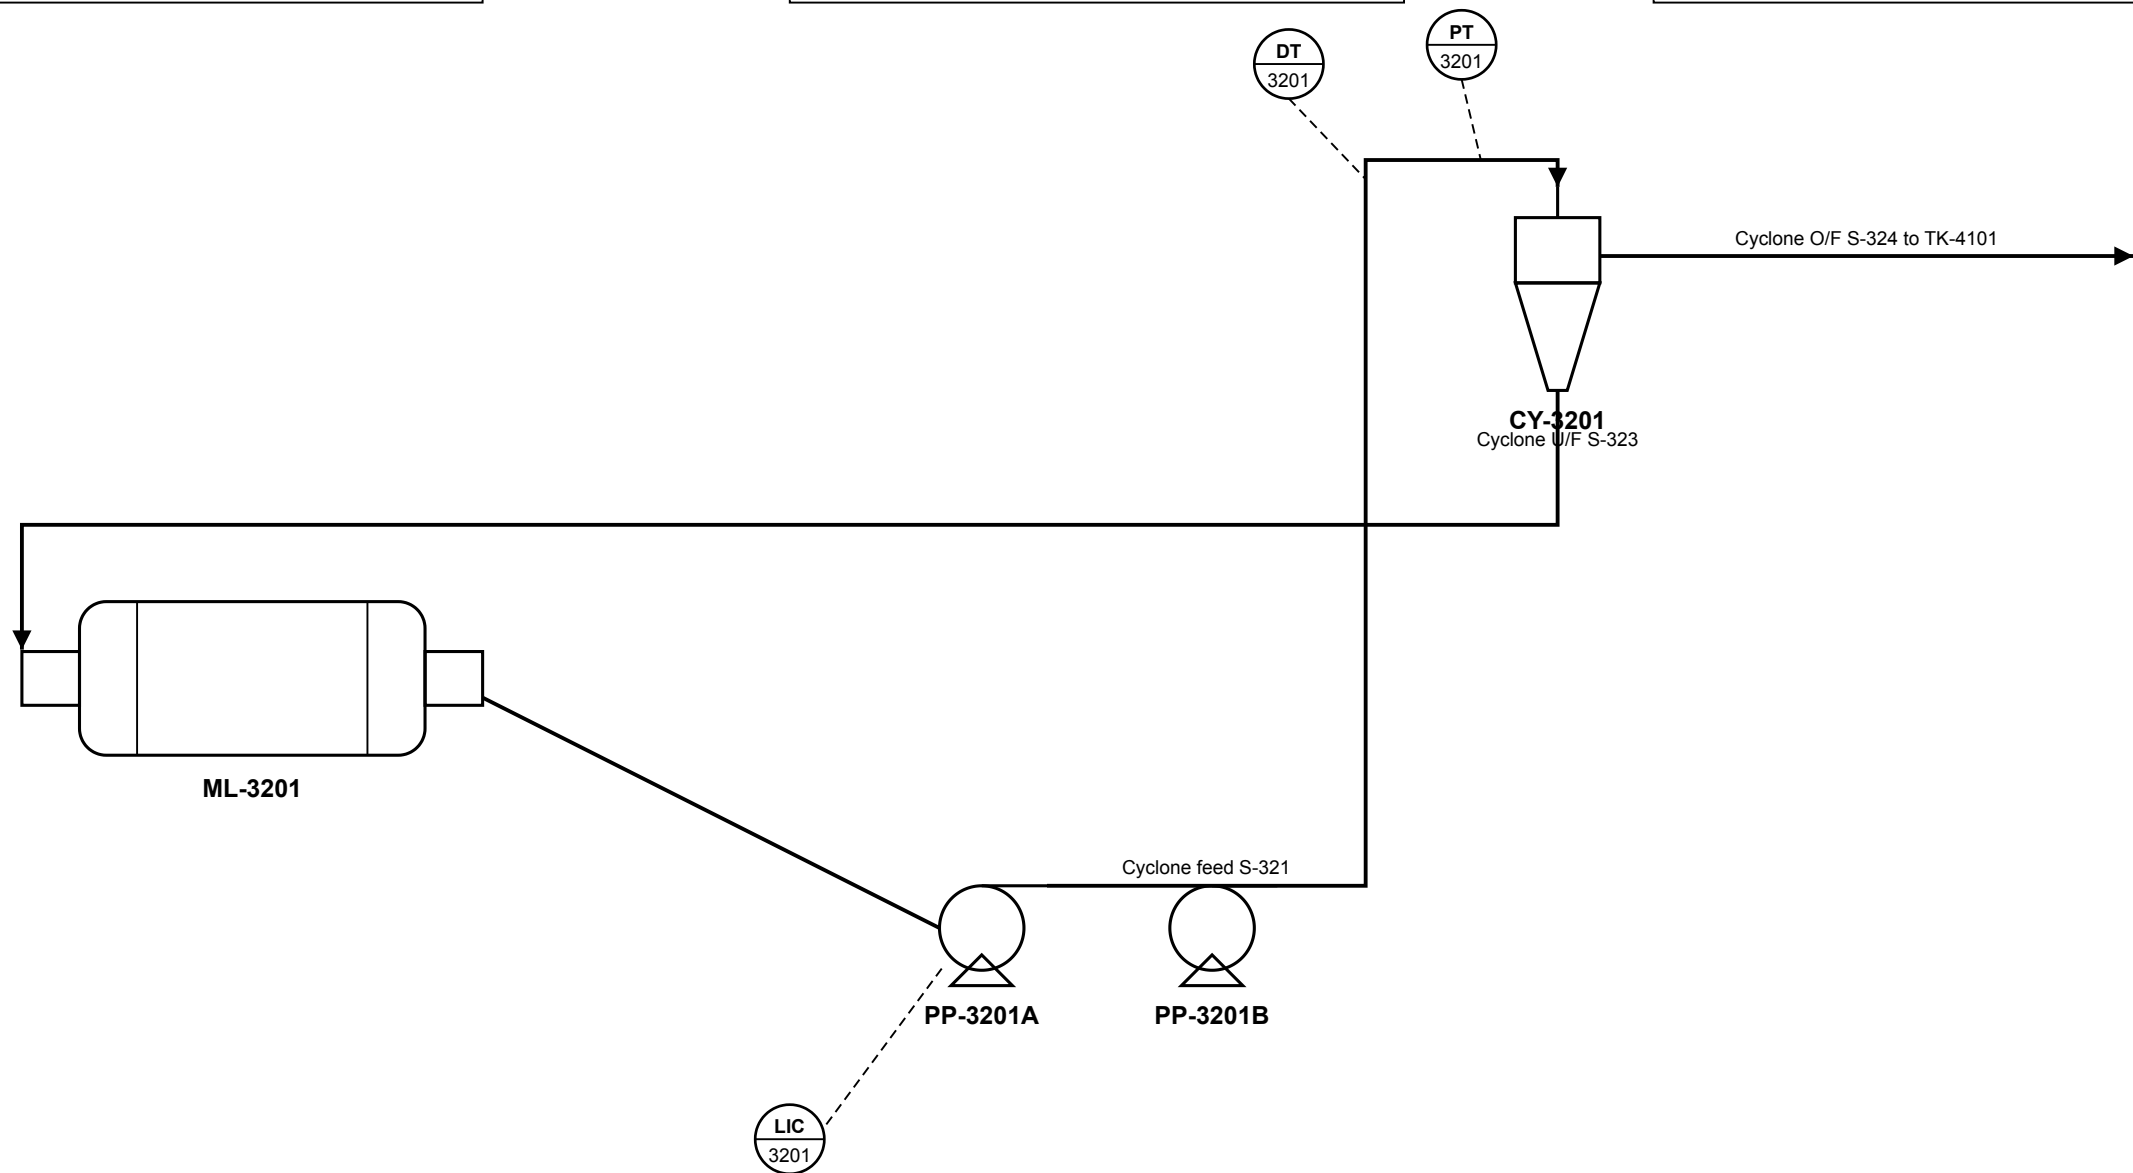

- NOTES**
1. Cyclone feed hopper level LIC-3201 controls pump speed.
 2. Standby pump PP-3201C identical to A/B.
 3. Density DT-3201 is nuclear gauge - radiation permit applies.

Cymbal Copper Pty Ltd (fictional) Ridgeback Concentrator - Project RB-4410		SYNTHETIC DEMO DRAWING
PIPING & INSTRUMENTATION DIAGRAM BALL MILL ML-3201 & CYCLONE CLUSTER CY-3201		
DWG No. RB-4410-PID-32-001		
		REV B