


TK-4501 PAX MIXING TANK
40 m3, 316L
Enclosed room, extraction FN-4501

TK-4511 FROTHER STORAGE TANK
Reagent: Polyglycol ether frother (DF-250 type)
30 m3

TK-4521 MILK-OF-LIME TANK
150 m3, 20 % w/w
From slaker SL-4521

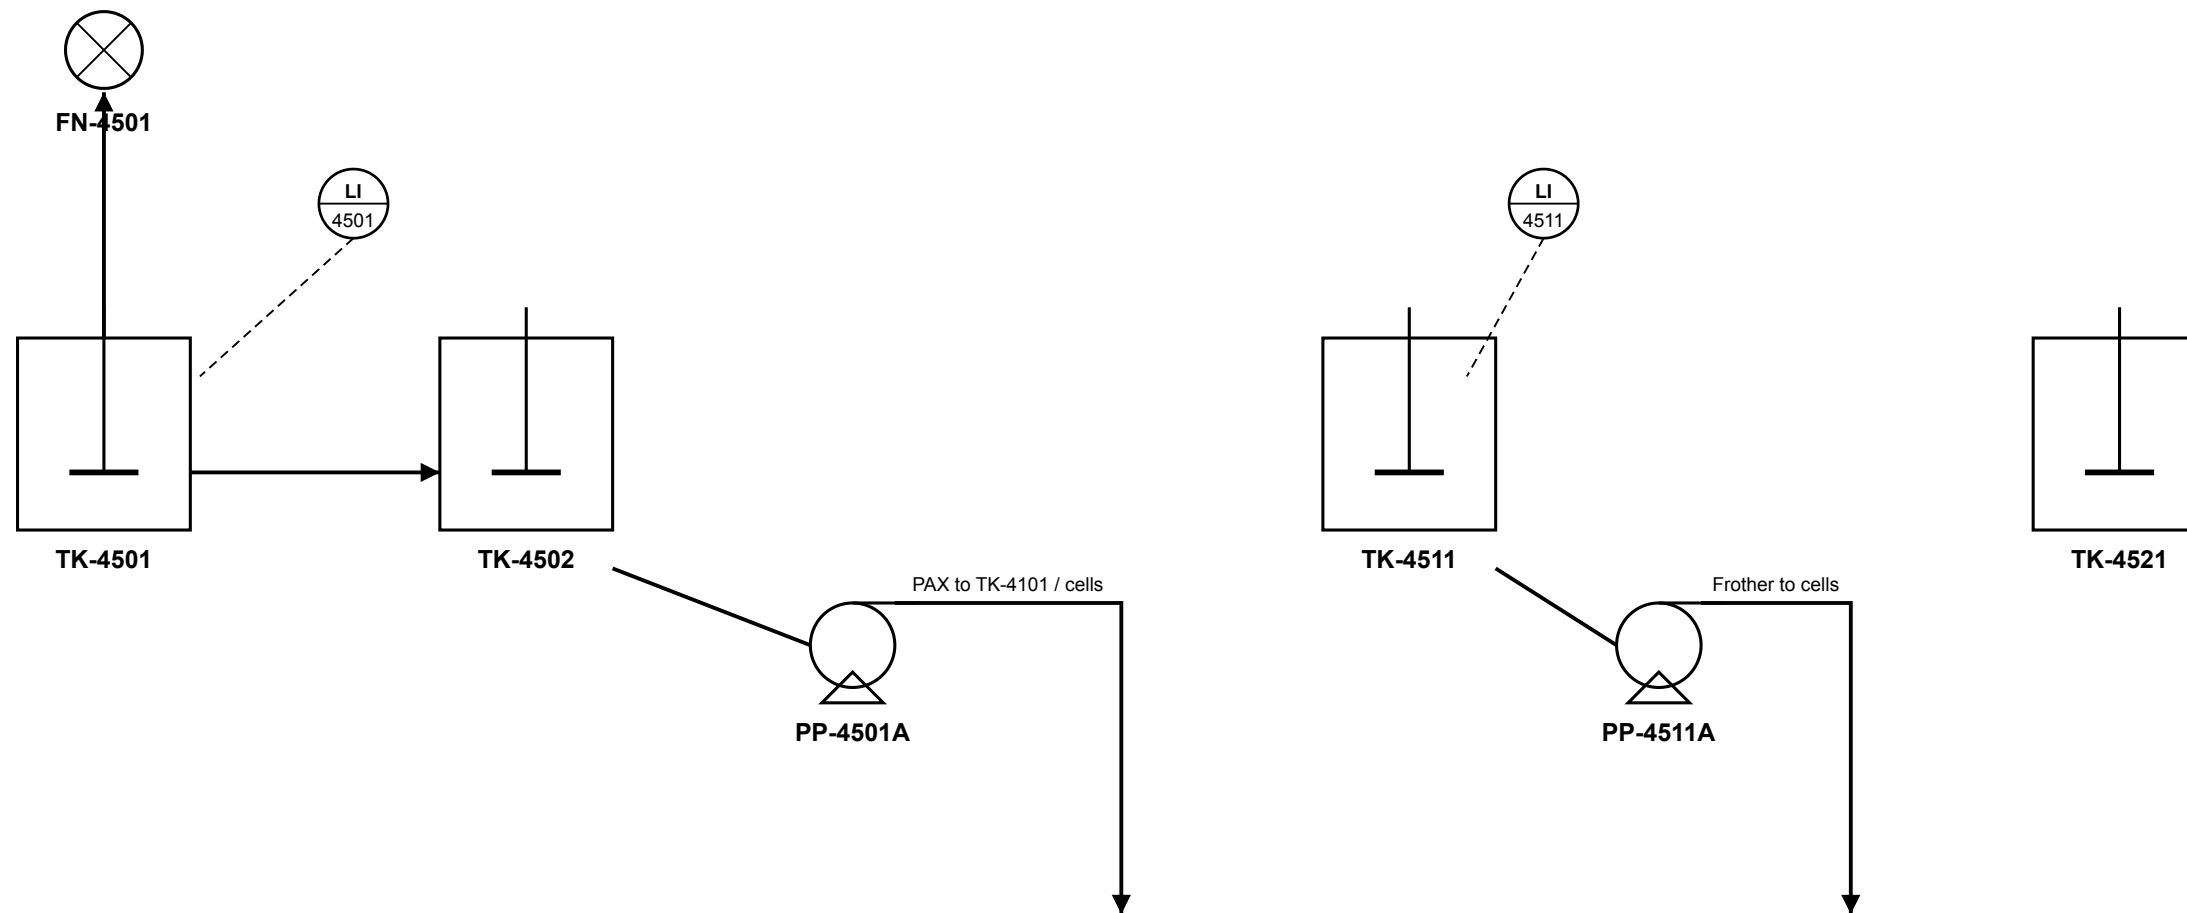

NOTES

1. PAX mixing room ventilation by FN-4501 (continuous).
2. Frother tank bunded; area classification per RB-4410-STD-HAC-001.
3. Lime slaker SL-4521 on vendor drawing.
4. Reagent dosing rates per operating manual RB-4410-OM-001.

Cymbal Copper Pty Ltd (fictional)
Ridgeback Concentrator - Project RB-4410

SYNTHETIC DEMO DRAWING

PIPING & INSTRUMENTATION DIAGRAM
REAGENTS - XANTHATE, FROTHER & LIME

DWG No. RB-4410-PID-45-001

REV B