


TH-6101 TAILINGS THICKENER
Diameter: 60 m
U/F 62 % w/w

PP-6101A/B/C TAILINGS PUMPS (SERIES)
Rated: 2,576 m3/h
Stage-3 discharge: 34 bar(g)
Stage-3 casing design: 4.0 bar(g)

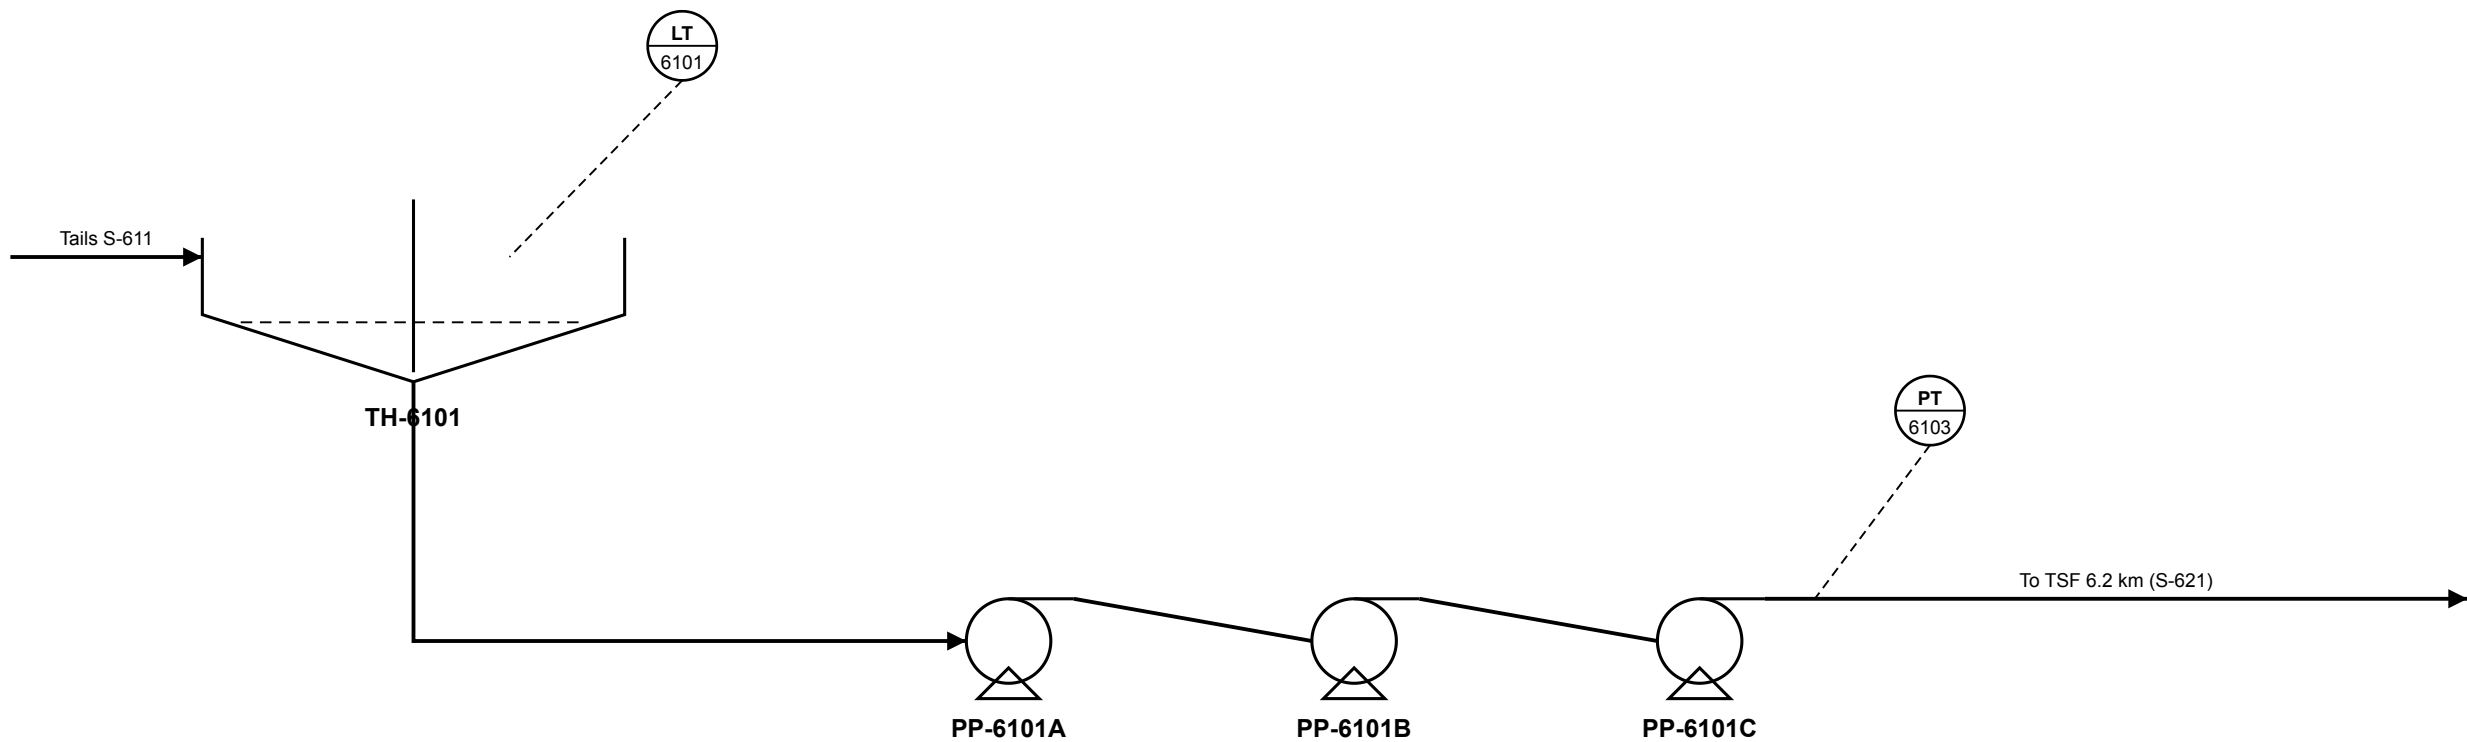

- NOTES**
- 1. PT-6103 PAHH trips all three pumps via SIF-6101 (SIL 2).
 - 2. Pipeline pressure rating per RB-4410-STD-TSF-002.
 - 3. Flushing water connections not shown.

Cymbal Copper Pty Ltd (fictional) Ridgeback Concentrator - Project RB-4410		SYNTHETIC DEMO DRAWING
PIPING & INSTRUMENTATION DIAGRAM TAILINGS THICKENING & PUMPING TO TSF		
DWG No. RB-4410-PID-61-001		
		REV B